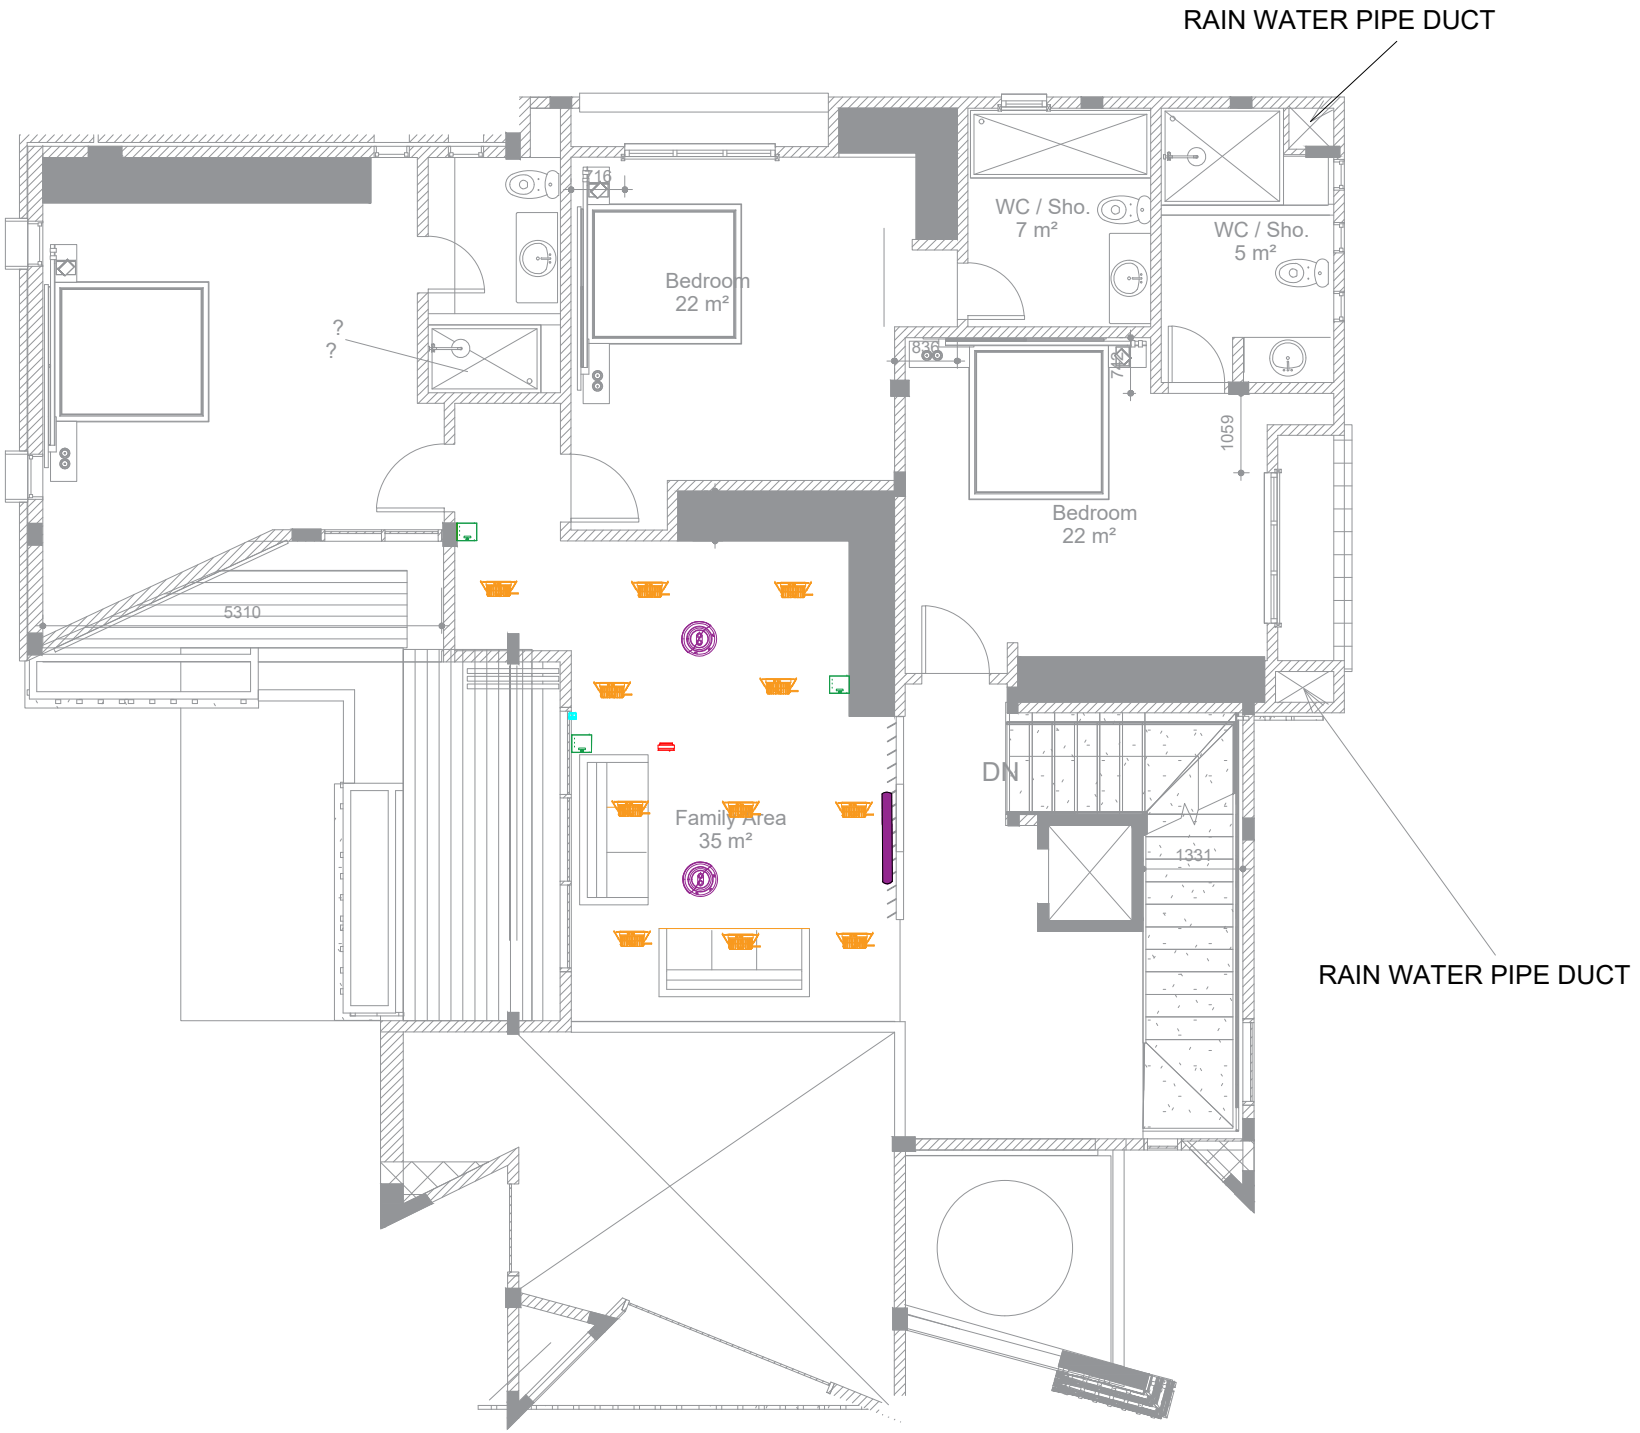


NOTES

This drawing is for reference only. Verify all dimensions and conditions onsite before installation.

Where site conditions differ from this drawing, the actual site layout shall take precedence , and the technician shall use sound engineering judgement.

Contractors and technicians are to locate and identify existing services on site and protect them from damage throughout the duration of the work.

SYMBOL	DESCRIPTION
	LOXONE PRESENCE SENSOR
	LOXONE LED SPOTLIGHT
	LOXONE CEILING SPEAKER
	LOXONE SMOKE DETECTOR
	LOXONE RGBW STRIPLIGHT
	LOXONE COMPACT DIMMER AIR
	LOXONE TOUCH PURE FLEX
	NANO 2 RELAY
	LOXONE 10 in WALL DISPLAY

PROJECT NAME: WILLIAMS RESIDENCE

CLIENT: HUMPHREY & SHIRLEY

LOCATION: EAST LEGON

Drawing Title: LIGHTING - LANDSCAPE PLAN

Designer

INTELLIGENT BUILDING SOLUTIONS

ibs
INTELLIGENT BUILDING SOLUTIONS

Drawn: M.A.A.B

Checked: EDWARD QUARSHIE

Date: 21/10/2026

Scale:

Ref No:

PROJECT	REV.	CODE	SHEET SIZE
WILLAIMS RESIDENCE			

drawing no: SM-WR-2026